



CONCEPT, NOT FOR FABRICATION

FieldCell · github.com/BoujeeEnjinia1701/fieldcell

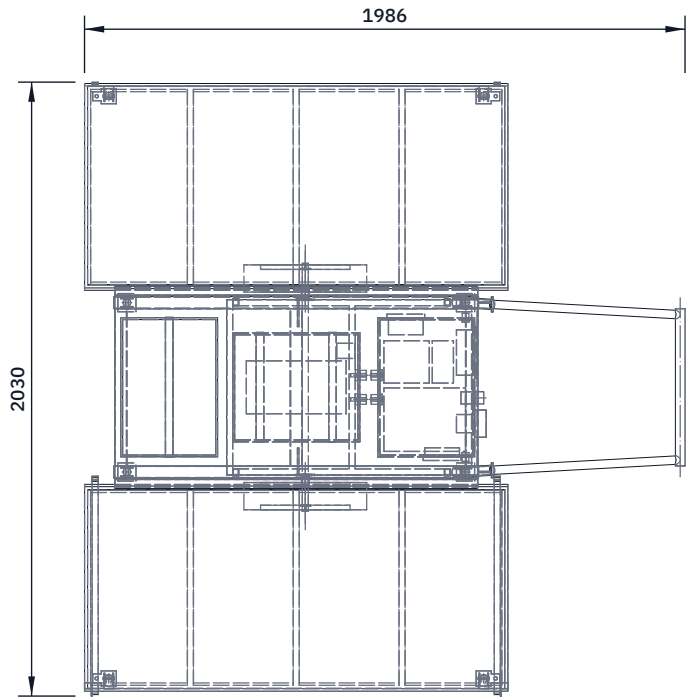


TOP VIEW

Scale 1:25; looking down (along -Z)

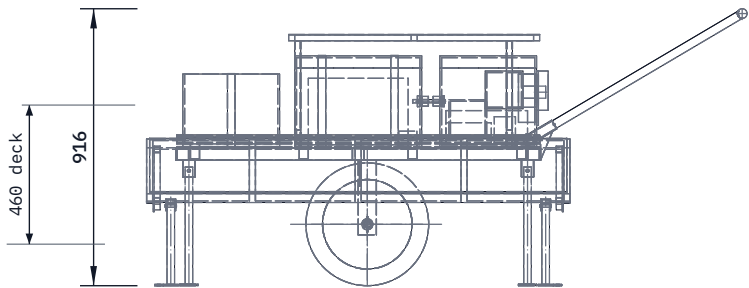

FRONT VIEW


Scale 1:25; looking at the front (along +Y)

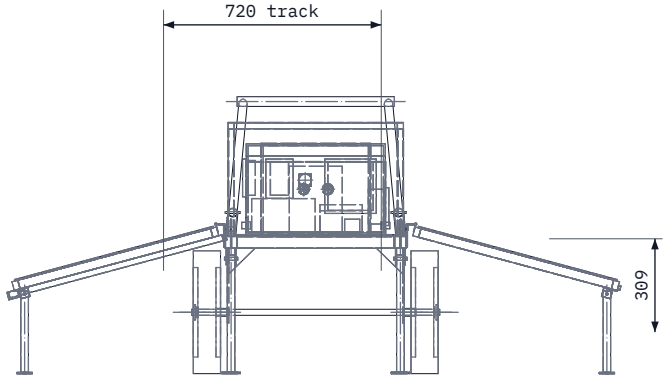

RIGHT VIEW

Scale 1:25; looking at the right side (along -X)

REV	DESCRIPTION	DATE	BY
P1	Preliminary GA for TRL 3 (from cad/src/model.py)	2026-09-25	AC
P2	Hinge spacer +20 mm, sun shade added (DDR-002)	2026-09-25	AC
P3	Layout and labels tidied	2026-09-30	AC
P4	Constructable design (DDR-003): tabs, sockets, clevises, tie bars, shade uprights	2026-10-01	AC

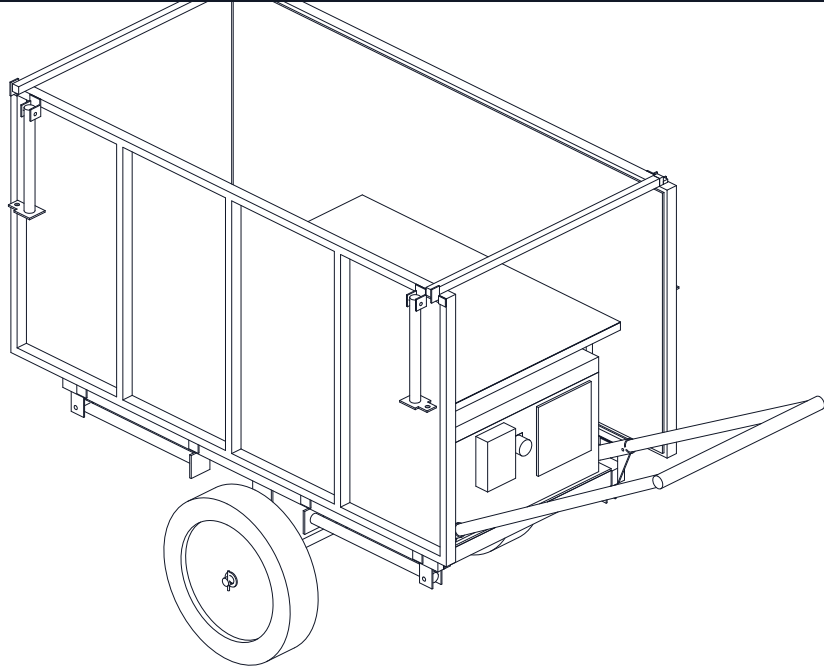

ISOMETRIC VIEW, STOWED FOR TRAVEL

Not to scale; seen from the front right and above, about 30 deg elevation

MAIN DIMENSIONS AND INTERFACES (MM)

Deployed 1,986 L x 2,030 W x 916 H; wingspan 2,012
Stowed, handle off: 1,400 x 830 x 1,220
Frame 1,200 x 600, 40 x 40 x 1.5 steel tube; deck 460 parked
Wheels 406 dia., track 720; axle 30 toward handle
Hinge pin Y +/-330, Z 495; wings 15 deg below horizontal
Hinge on 20 x 20 angle, welded tabs; wing to tyre 28
Sun shade on 4 uprights (item 18); tie bars (item 19)
Outlet face toward handle; grip at Z 900
Mass about 80.0 kg (FCL-CAL-001); 2 x 200 W PV, 1.28 kWh
Third-angle; front view from -Y, right view from +X

FIELDCELL

github.com/BoujeeEnjinia1701/fieldcell

General arrangement

DRAWING NO. FCL - DWG - 002			REV P4	SHEET 1 of 1	SIZE ANSI B
SCALE 1:25	UNITS mm	PROJECTION 	DATE 2026-10-01	DRAWN Amish Chadha	

MATERIAL / NOTES
Welded steel frame, IP65 and IP54 enclosures; see bom/bom.csv. PRELIMINARY, NOT FOR FABRICATION